


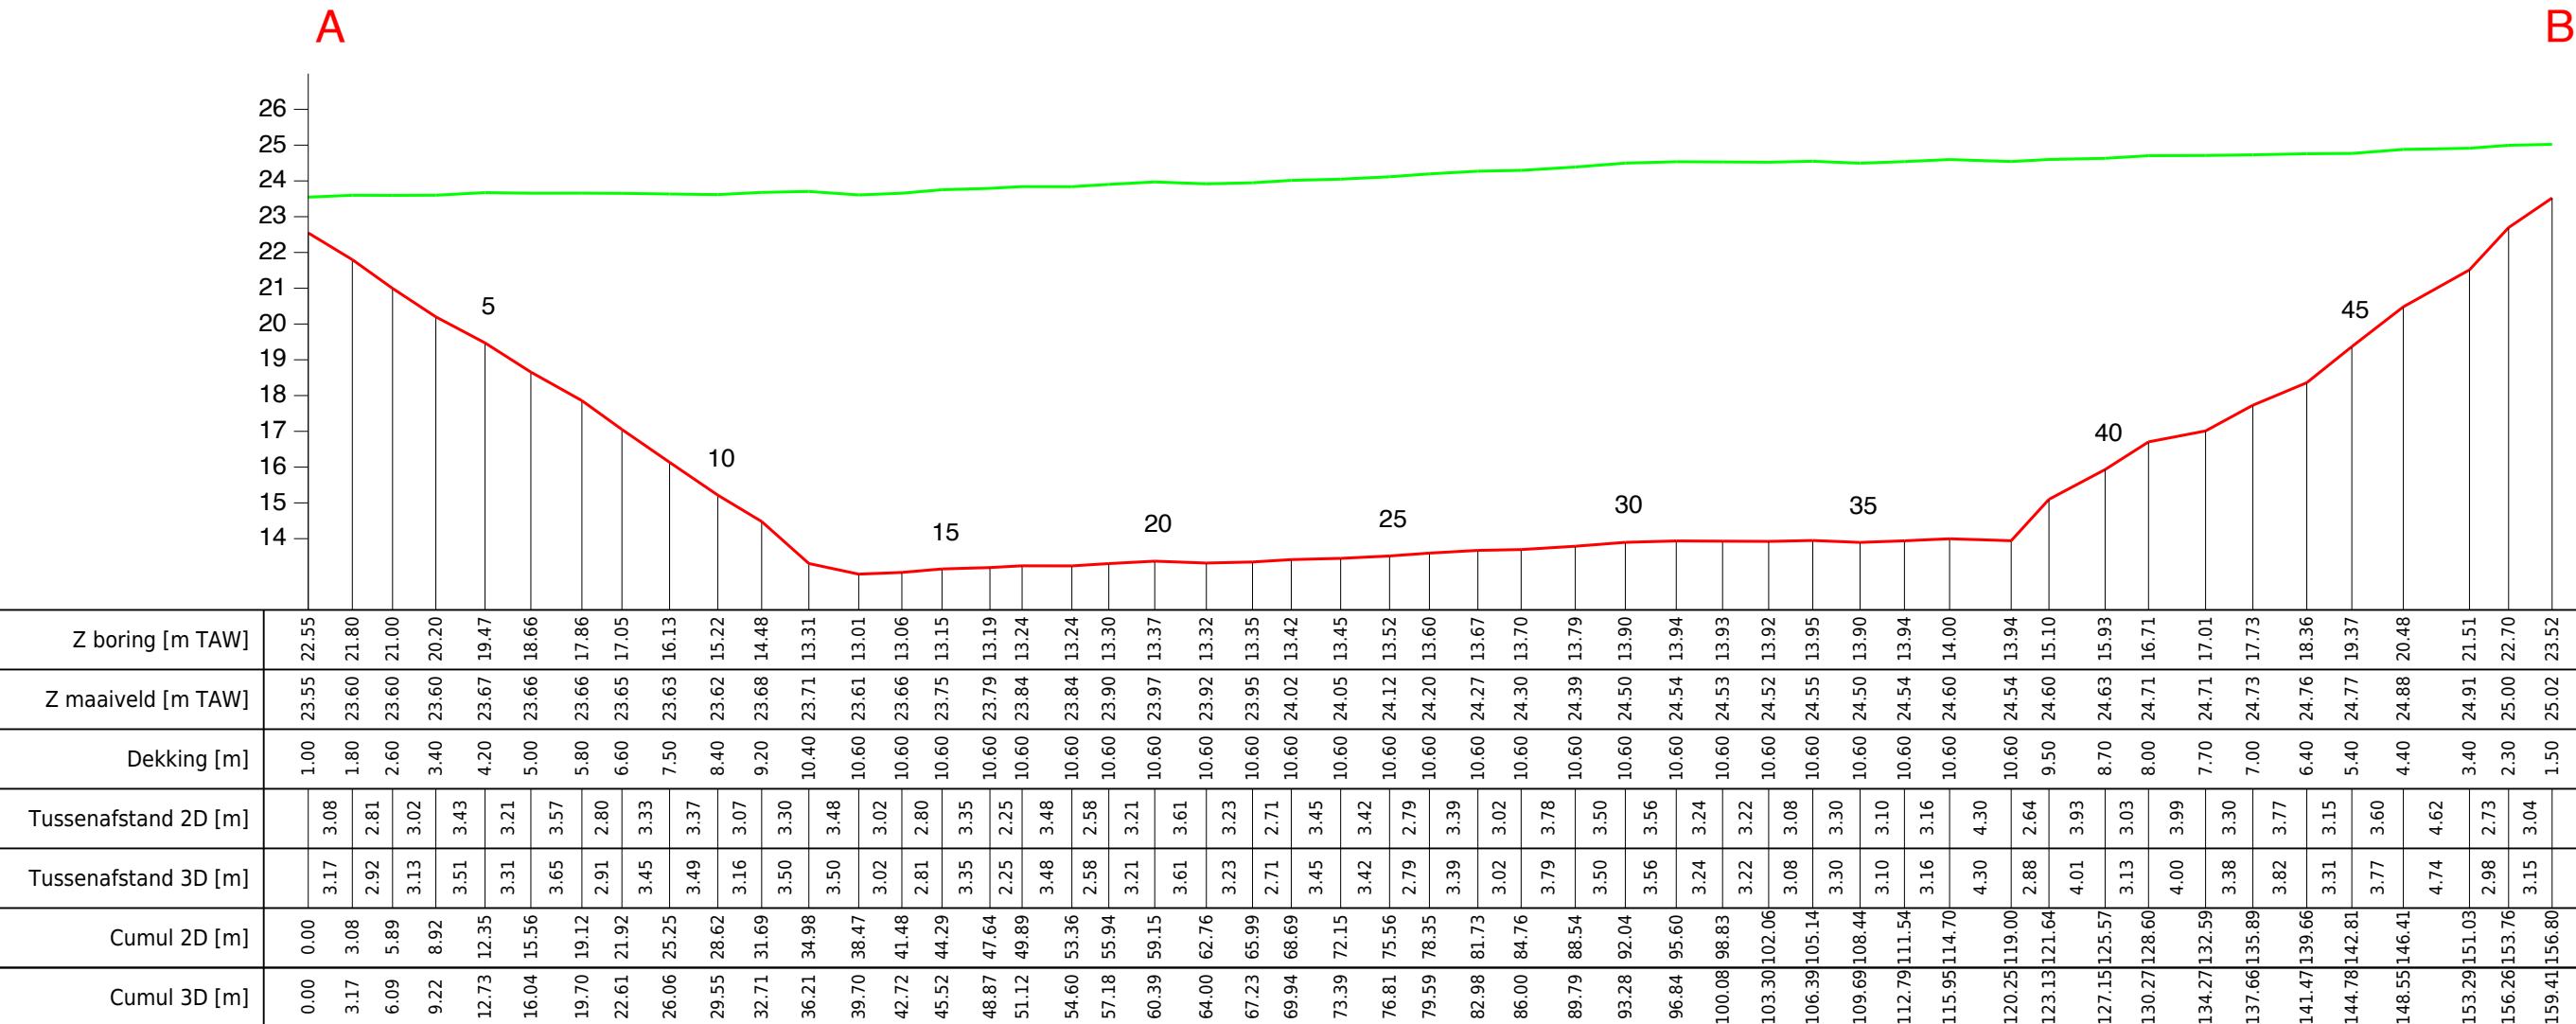

LIGGINGS- en DEKKINGSTABEL - Lambert 72 - TAW					
Punt	X	Y	Z	Dekking	Info
A	80749.48	169796.63	22.55	1.00	Intredepunt
2	80751.15	169794.04	21.80	1.80	
3	80752.68	169791.68	21.00	2.60	
4	80754.21	169789.07	20.20	3.40	
5	80755.94	169786.11	19.47	4.20	
6	80757.45	169783.28	18.66	5.00	
7	80759.11	169780.12	17.86	5.80	
8	80760.30	169777.59	17.05	6.60	
9	80761.82	169774.63	16.13	7.50	
10	80763.39	169771.65	15.22	8.40	
11	80764.95	169769.01	14.48	9.20	
12	80766.53	169766.11	13.31	10.40	
13	80768.21	169763.06	13.01	10.60	
14	80769.60	169760.38	13.06	10.60	
15	80770.84	169757.87	13.15	10.60	
16	80772.21	169754.81	13.19	10.60	
17	80773.04	169752.73	13.24	10.60	
18	80774.26	169749.47	13.24	10.60	
19	80775.13	169747.04	13.30	10.60	
20	80776.13	169743.99	13.37	10.60	
21	80777.19	169740.54	13.32	10.60	
22	80778.00	169737.42	13.35	10.60	
23	80778.60	169734.78	13.42	10.60	
24	80779.33	169731.40	13.45	10.60	
25	80779.94	169728.04	13.52	10.60	
26	80780.33	169725.28	13.60	10.60	
27	80780.72	169721.92	13.67	10.60	
28	80780.81	169718.90	13.70	10.60	
29	80780.67	169715.12	13.79	10.60	
30	80780.49	169711.62	13.90	10.60	
31	80780.47	169708.07	13.94	10.60	
32	80780.32	169704.83	13.93	10.60	
33	80780.10	169701.62	13.92	10.60	
34	80779.80	169698.55	13.95	10.60	
35	80779.82	169695.25	13.90	10.60	
36	80779.45	169692.17	13.94	10.60	
37	80779.08	169689.03	14.00	10.60	
38	80778.34	169684.79	13.94	10.60	
39	80777.76	169682.22	15.10	9.50	
40	80776.81	169678.41	15.93	8.70	
41	80775.92	169675.51	16.71	8.00	
42	80774.56	169671.76	17.01	7.70	
43	80773.54	169668.62	17.73	7.00	
44	80772.15	169665.12	18.36	6.40	
45	80770.95	169662.21	19.37	5.40	
46	80770.18	169658.69	20.48	4.40	
47	80769.30	169654.15	21.51	3.40	
48	80768.46	169651.55	22.70	2.30	
B	80767.45	169648.69	23.52	1.50	

ONTWIKKELD PROFIEL

Lengteschaal 1:500 Hoogteschaal 1:200



UITVOERDER		OPDRACHTGEVER		GESTUURDE BORING - PLAN PREBUILT	
KALE-TECH BV Langestraat 79 9240 Zele 0483 27 19 04 kale-tech@hotmail.com		JACOBS NV Nijverheidsweg 31 8540 Deerlijk 056/77 84 51 info@jacobs.be		Olekenbosstraat 9, 8570 Anzegem	
		REFERENTIES		LIGGING	
		25035678		Punt A Olekenbosstraat 9	
		Lengte boring= 159.41 m		Punt B Reynaertstraat 1	
		DATUM UITVOERING (pilot)		UITVOERING / OPMETING	
		Nog te bepalen		Gestuurde boring RTK + walkover	
		INHOUD		Planonline doc: nr. plan_12_20260907_A1_290537ff-e7ca-412b-9daa-10e43b02e932e.pdf	
		1x0125			